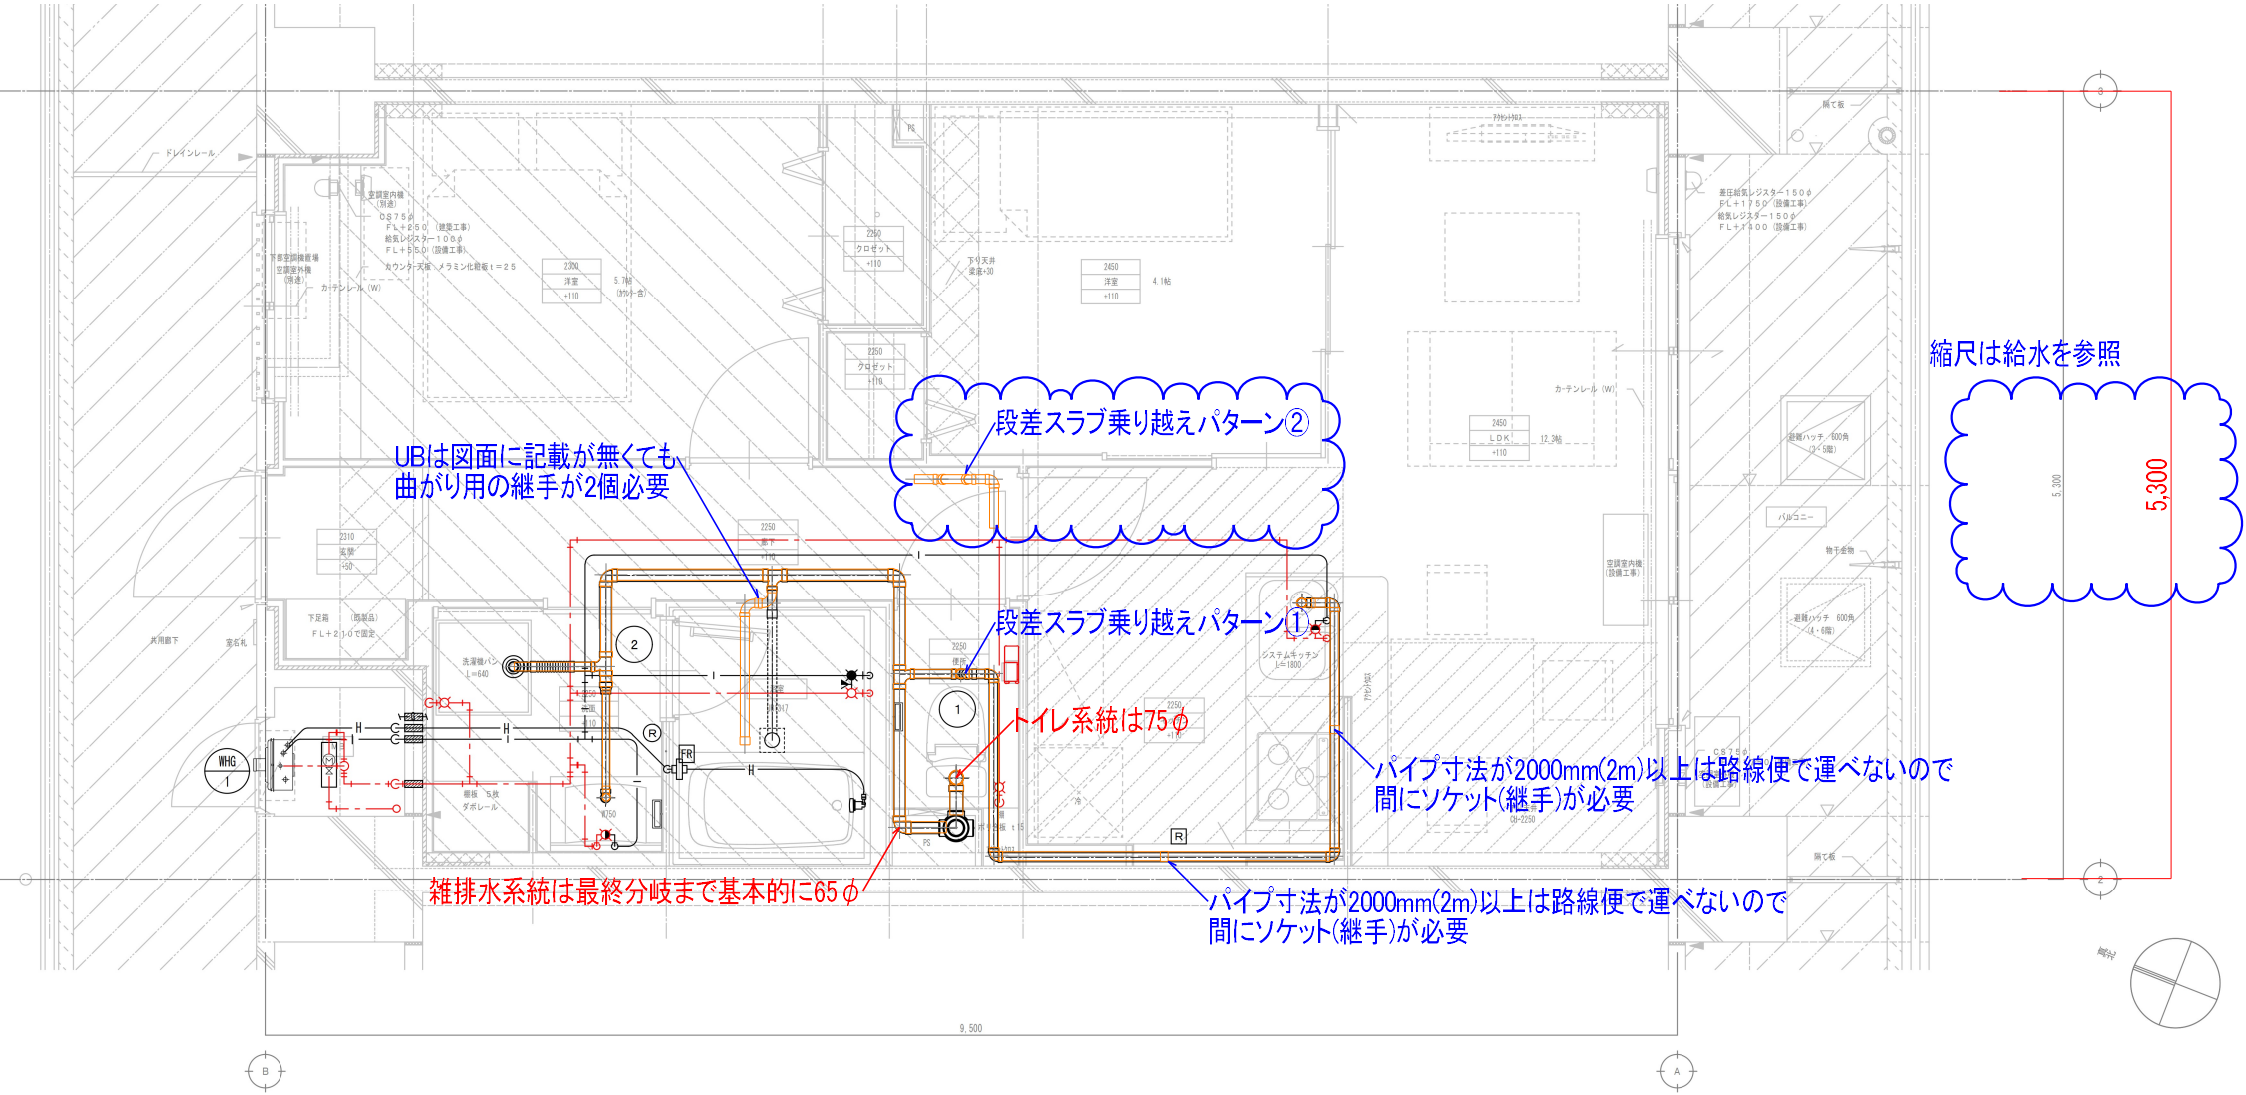

(注記) 配管サイズは下記による		
名　称	区　間	口　径
給　水	全て	20HI
給　湯	2カ所合流以降	16φ
	UB・キッチン	13φ
	洗面化粧台	
差し湯	全て	13φ
排　水	大便器	75
	洗面化粧台・手洗器	40
	UB・洗濯機パン	50
	キッチン	
	2カ所合流以降	65

口径の指定あり

注記	●印適用　[図面注記部分は除く]
●	1. 配管ルートは、施工図にて決定のこと。
●	2. スラブ下がり　SL-130
●	3. 給湯・差し湯配管は架橋ポリエチレン管又はポリブデン管とする。
●	4. ガス給湯器は開口及び可燃物から150mm以上の離隔をとること。
○	5. 最下階集合管より横枝管1m以上耐火二層管(FDP)にて施工のこと。

記号	凡例
	洗濯パン用フレキ50（樹脂製　内部平滑型）
	UB貫通継手
	区画貫通部耐火処置
	風呂アダプター
R	メインリモコン　リモコンコード（電気工事空配管に入線）
FR	風呂リモコン　リモコンコード（電気工事空配管に入線）
R	浴乾用リモコン　リモコンコード（電気工事空配管に入線）

器具表			
NO	名　称	参考品番	附　属　品
1	洋風大便器	CFS371A	SH371BA(タンク)TCF2213E(洗浄便座)
			SC-613-XC(紙巻器)SC-451-XN(タオル掛)
2	ユニットバス	建築工事	※　サーモ付混合栓
	洗濯機パン	建築工事	
	洗濯パン用水栓	SP1100N（TBC）	緊急止水弁付横水栓
	洗面化粧台	建築工事	※止水栓×2 本工事
	タオル掛け	SC-451-XN	※三面鏡の開閉時に干渉しない位置に設置すること。
3	キッチン	建築工事	
	キッチン水栓	建築工事	※止水栓×2 本工事
※　混合栓は逆止弁内蔵型又は取付けとする（2バルブは除く）			