A図面平面図

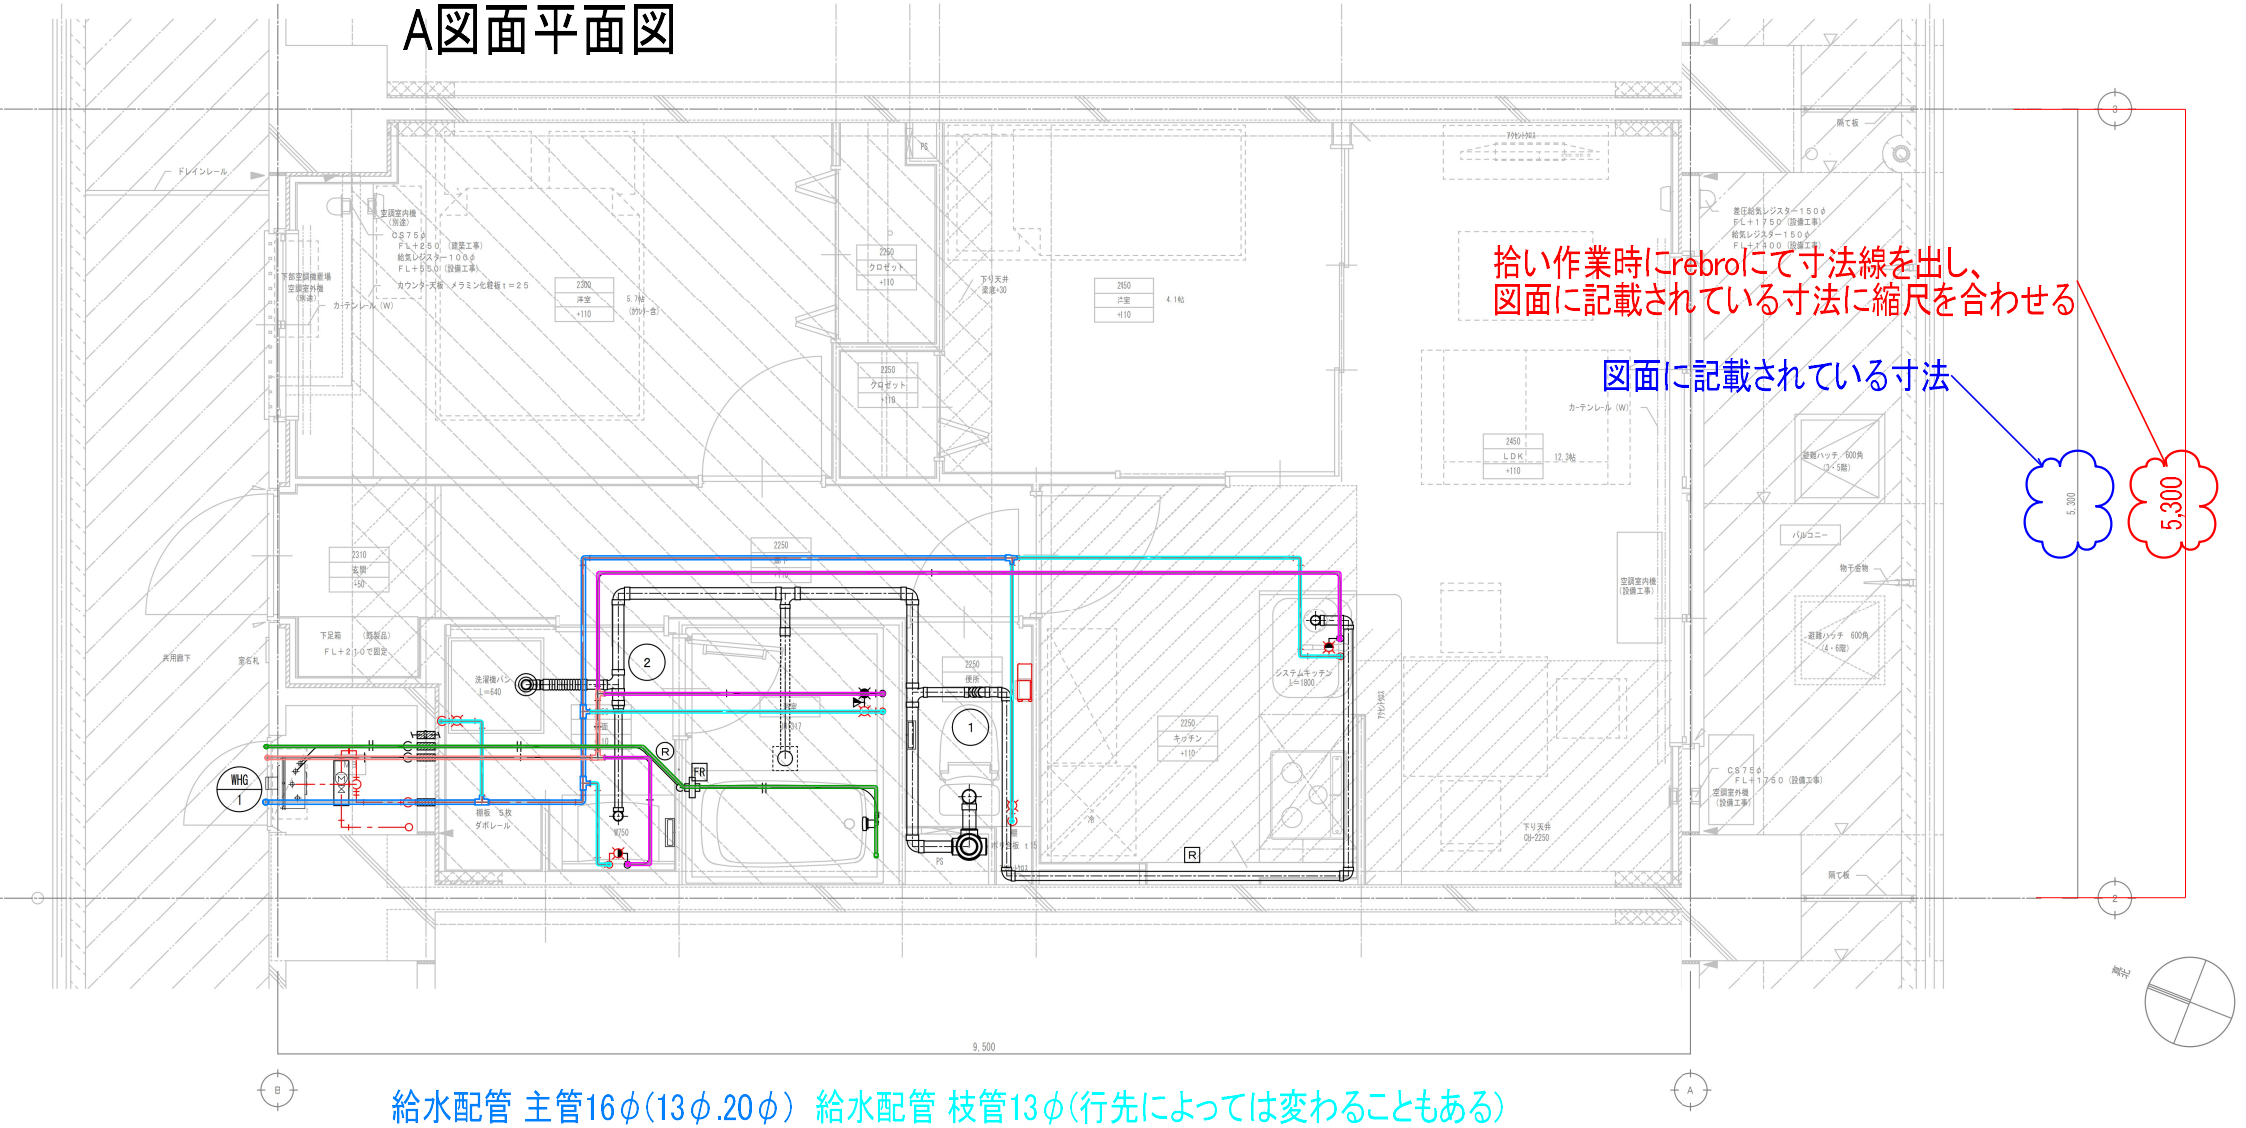

給水配管 主管16φ(13φ.20φ) 給水配管 枝管13φ(行先によっては変わることもある)

給湯配管 主管16φ(13φ.20φ) 給湯配管 枝管13φ(行先によっては変わることもある)

追い焚き配管 主管13φ1本(基本的には10φ×2本)

(注記) 配管サイズは下記による		
名 称	区 間	口 径

器具表			
N O	名 称	参 考 品 番	附 属 品