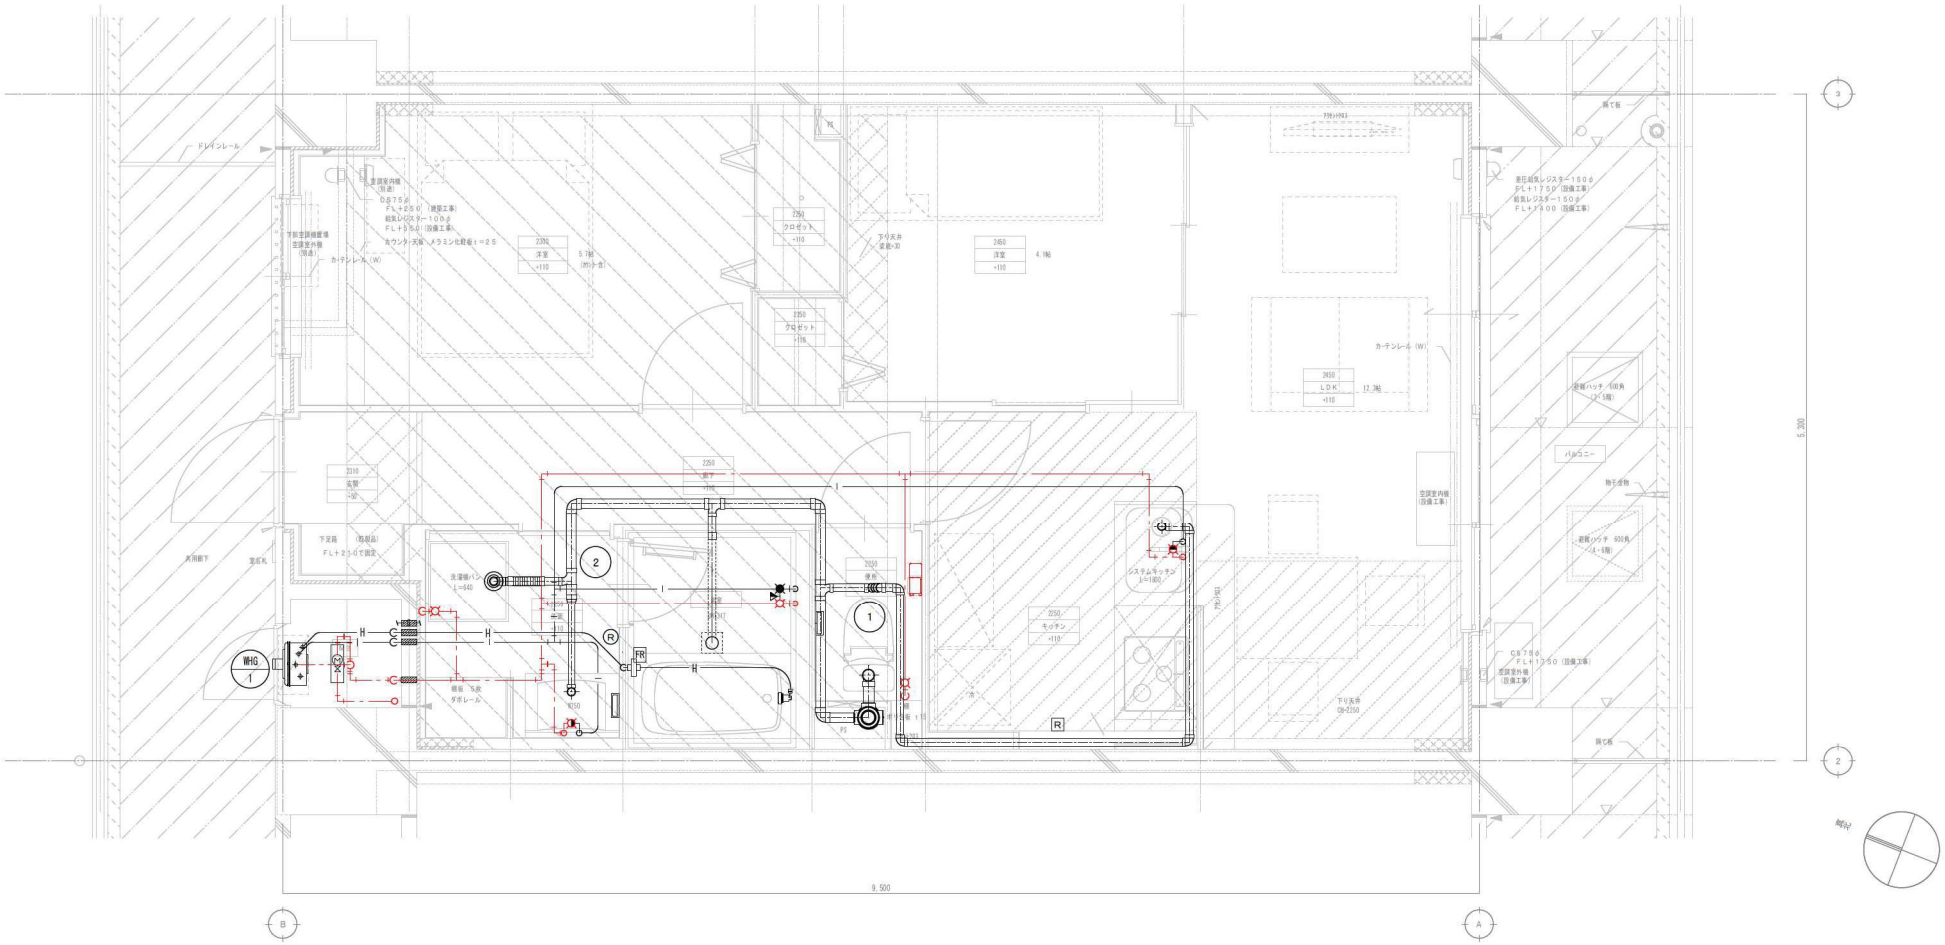

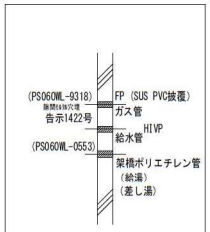

区画貫通部施工要領

(注記) 配管サイズは下記による		
名 称	区 間	口 径
給 水	全て	20HI
給 湯	2カ所合流以降	16φ
	UB・キッチン	13φ
	洗面化粧台	
差し湯	全て	13φ
排 水	大便器	75
	洗面化粧台・手洗器	40
	UB・洗濯機パン	50
	キッチン	
	2カ所合流以降	65

注記	●印適用 [図面注記部分は除く]
●	1. 配管ルートは、施工図にて決定のこと。
●	2. スラブ下がり SL-130
●	3. 給湯・差し湯配管は架橋ポリエチレン管又はポリブデン管とする。
●	4. ガス給湯器は開口及び可燃物から150mm以上の離隔をとること。
○	5. 最下階集合管より横枝管1m以上耐火二層管(FDP)にて施工のこと。

記号	凡例
	洗濯パン用フレキ50 (樹脂製 内部平滑型)
	UB貫通継手
	区画貫通部耐火処置
	風呂アダプター
R	メインリモコン リモコンコード (電気工事空配管に入線)
FR	風呂リモコン リモコンコード (電気工事空配管に入線)
Ⓡ	浴乾用リモコン リモコンコード (電気工事空配管に入線)

器具表			
NO	名 称	参考品番	附 属 品
1	洋風大便器	CFS371A	SH371BA(タンク)TCF2213E(洗浄便座)
			SC-613-XC(紙巻器)SC-451-XN(タオル掛)
2	ユニットバス	建築工事	※ サーモ付混合栓
	洗濯パン	建築工事	
	洗濯パン用水栓	SP1100N (TBC)	緊急止水弁付横水栓
	洗面化粧台	建築工事	※止水栓×2 本工事
	タオル掛け	SC-451-XN	※出面後の開閉時に干渉しない位置に設置すること。
3	キッチン	建築工事	
	キッチン水栓	建築工事	※止水栓×2 本工事

※ 混合栓は逆止弁内蔵型又は取付けとする (2バルブは除く)

・ ・	・ ・
・ ・	・ ・
・ ・	・ ・

©TakaMatsu 本資料、パース、図面等の著作権は髙松建設に帰属します。

NOTE

髙松建設 一級建築士事務所

承認			担当	本部長
近藤	酒井	田坂	南	山部

一級建築士第334877号 山部隆浩
一級建築士第390603号 設備設計一級建築士第6890号 中山潤也

西九条・是永グループ本社マンションⅡ新築工事

TITLE 機械設備工事
給排水衛生設備 A1タイプ (3-6階) 平面詳細図

SCALE A2 1:30 A3 1:42.4

M-10