管種、口径など記載

縮尺調整

給水設備　専用部内の仕様（全タイプ共通）　⊙ 印：採用

	部位・名称	仕様
⊙	ＭＢ～給湯器（ＭＢ内設置）	⊙ポリブデン管 20
⊙	ＭＢ～給水メイン管	⊙ポリブデン管 20
⊙	給水メイン管～各給水栓の給水管	⊙ポリブデン管 13
⊙	給湯器～給湯メイン管	⊙ポリブデン管 16
⊙	給湯メイン管～各給湯栓の給湯管	⊙ポリブデン管 13
⊙	ＵＢ天井部ミストカワック用	・ポリブデン管10Aボウズ　⊙GV, CV 15A

給水・給湯設備　注記（全タイプ共通）

⊙	給水管・給湯管は（⊙天井配管　・床下配管）とする
	（・天井ヘッダー方式　⊙工場融着先分岐方式（全配管保護管付とする）））
⊙	キッチン, 洗面化粧台 給水・給湯 止水栓取付共
・	キッチン, 洗面化粧台 給水・給湯 水栓取付部ボックス設置
⊙	キッチン, 洗面化粧台の混合水栓は建築工事とする
⊙	キッチン下にて給湯分岐バルブ設置，機器接続含む（食洗器設置）

サニタリーベンド等、一部継手は不要(ダイポリ手配不可)

→エルボと形が酷似している。いっそエルボとして拾う？

排水設備　専用部内の仕様（全タイプ共通）　⊙ 印：採用

	部位・名称	仕様
⊙	キッチンからの排水横引き管	⊙50
⊙	食洗器からの排水横引き管	⊙耐熱性硬質塩ビ管 25
⊙	ＵＢからの排水横引き管	⊙50
⊙	防水パンからの排水横引き管	⊙50
⊙	洗面化粧台からの排水横引き管	⊙40
⊙	便器からの排水横引き管（床上）	⊙75
⊙	便器からの排水横引き管（床下）	⊙75
⊙	合流後の配管サイズ	
	５０＋４０＝６５　５０＋６５＝６５	
	５０＋５０＝６５　トイレ　７５	
	排水横引管サイズは、２合流後６５とする	

排水設備　注記（全タイプ共通）

・	排水立管より（・半径　・実長）１ｍ以内は耐火二層管とし，以降硬質塩ビ管(VP)とする
	~~（・全階　・最下階住戸のみ）~~
⊙	食洗器排水：キッチン下にて排水分岐チーズ設置とし、排水分岐チーズ及び短管は
	耐熱塩ビ管ＨＴＶＰとする
⊙	防水パン接続は内面平滑フレキを使用とする（両端接着タイプ）
⊙	立管スリーブどうしの距離については消防40号省令緩和規定を順守のこと
⊙	洗面化粧台の排水接続部材は設備工事とする
⊙	その他　記入無きは特記仕様書参照とする

取消線

赤色の配管(設計図では黒)は食洗用HT-DV(耐熱)継手

→見分け方が困難？あらかじめ継手とパイプを登録しておく？

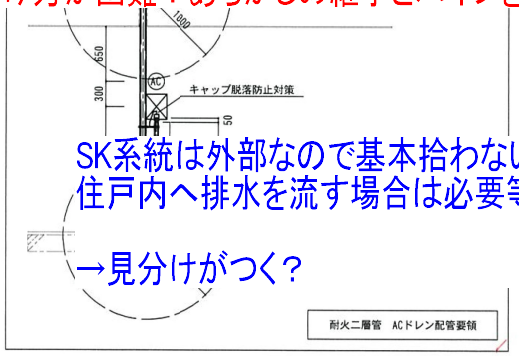

SK系統は外部なので基本拾わないが、
住戸内へ排水を流す場合は必要等…

→見分けがつく？

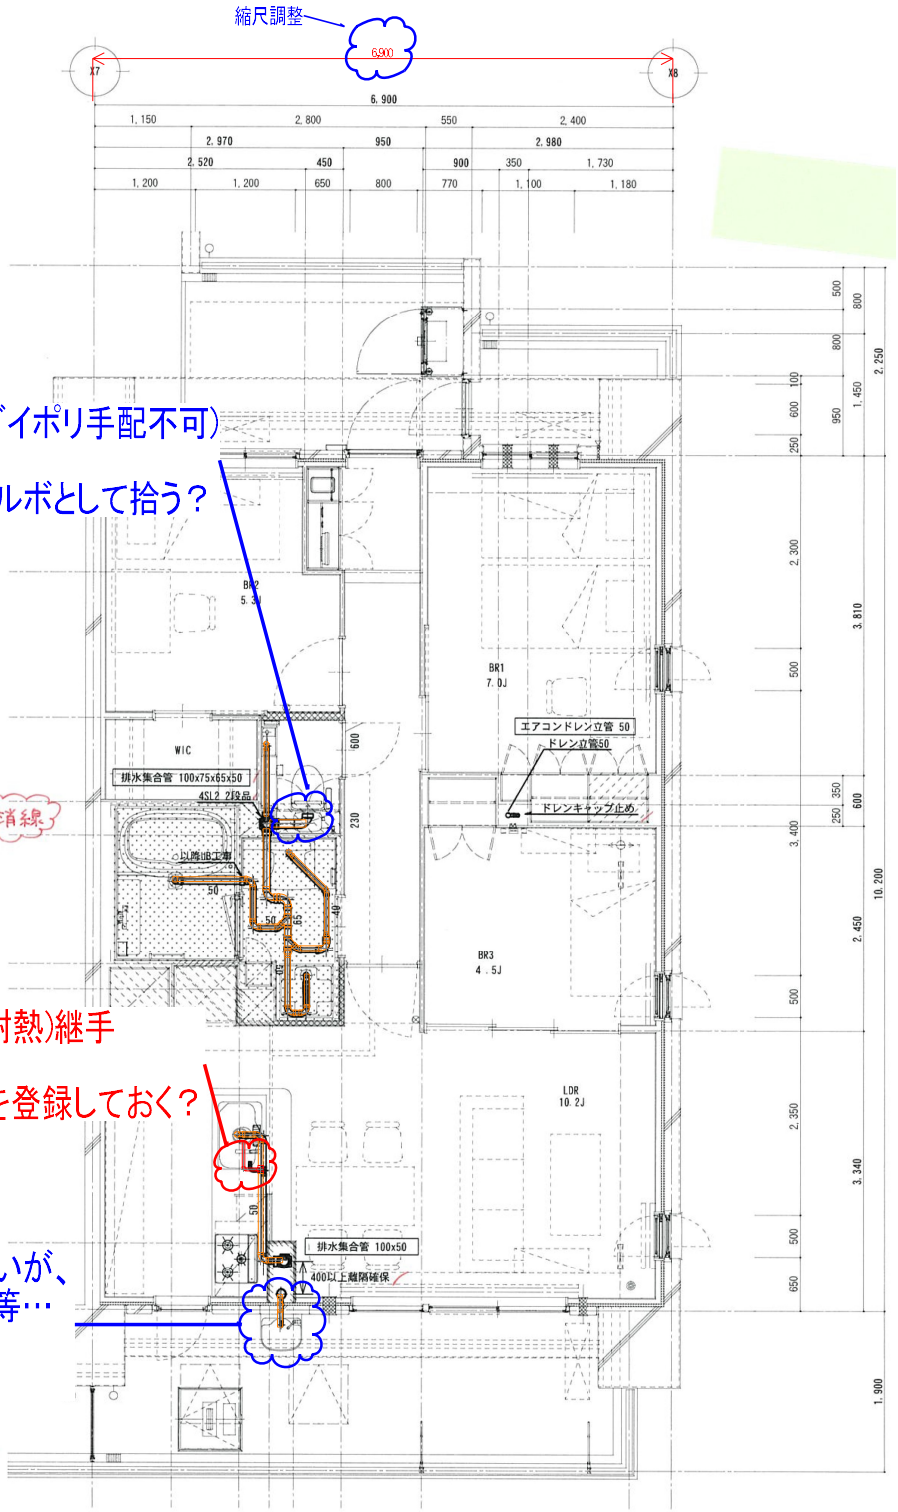

排水設備図