MB(メーターボックス)内は配管が省略されることが多い。

→MB内に入ったらパイプを+〇〇mというルールを作る？

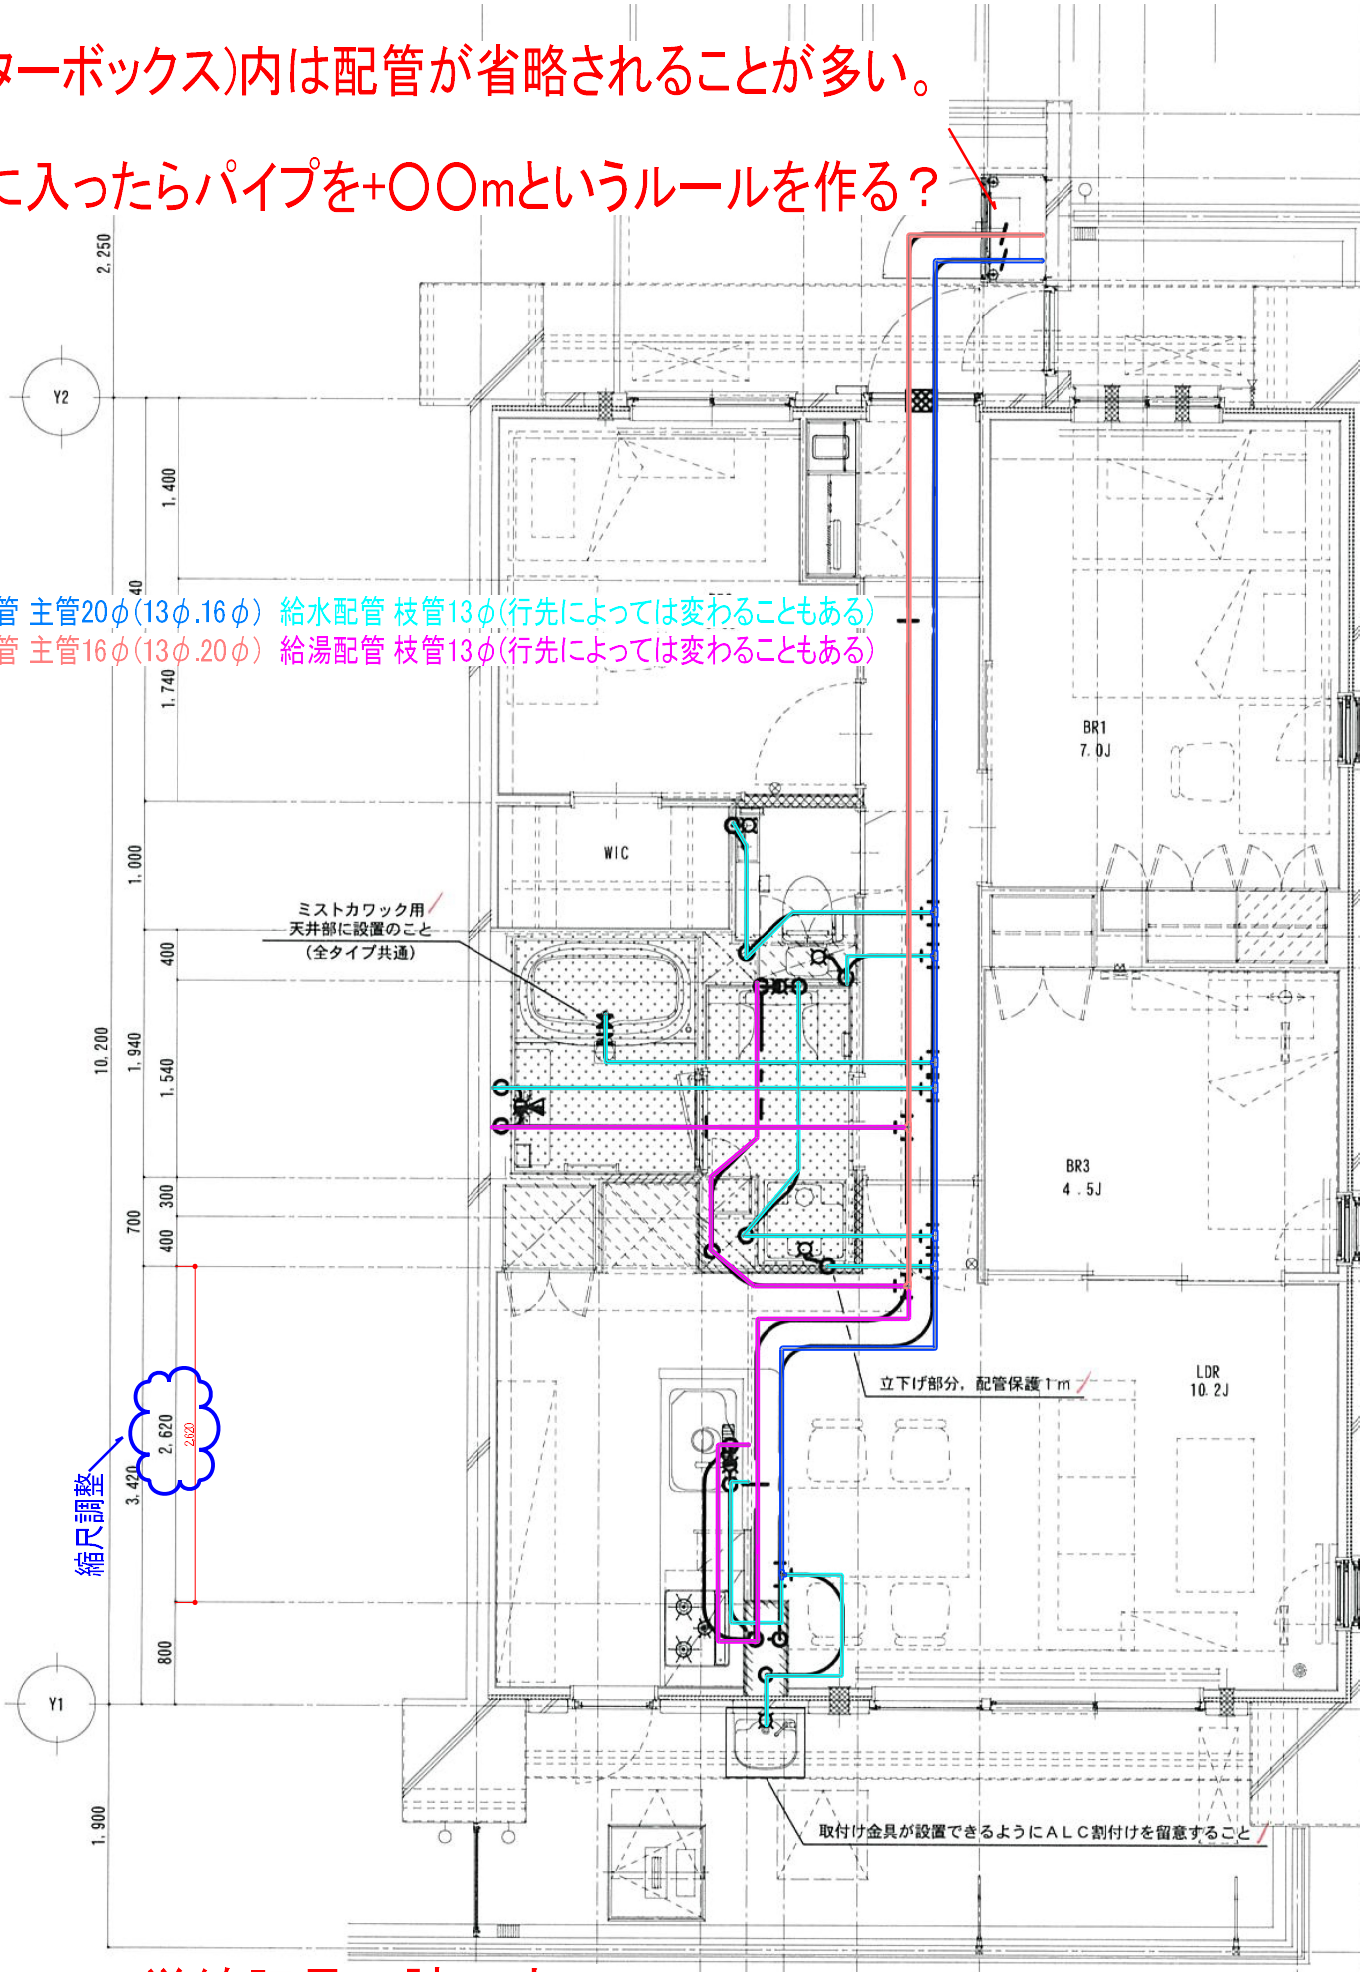

・単線記号の読み方
・天井配管の見分け方
別紙参照

給水設備図

代表となる設計者