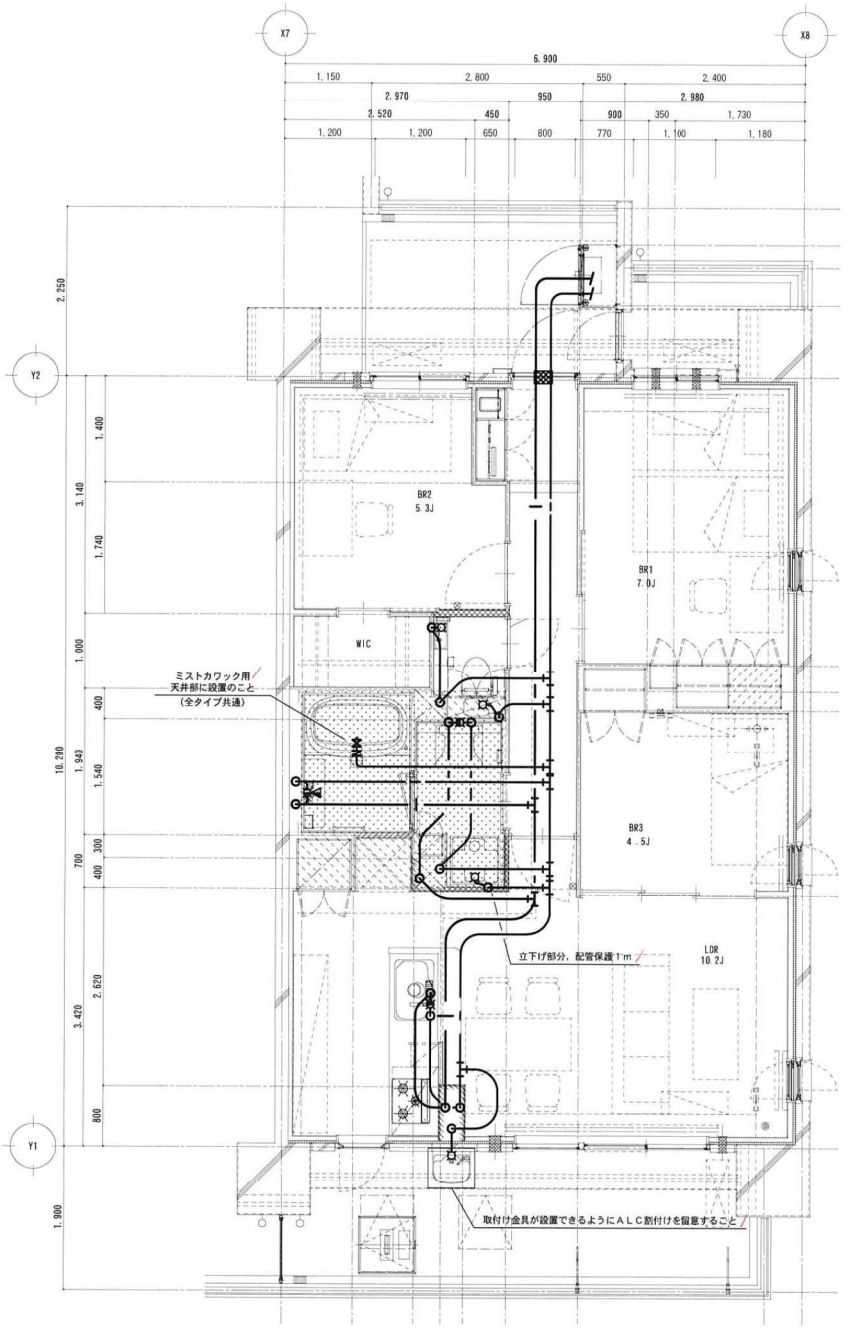

給水設備図

給水設備　専用部内の仕様（全タイプ共通）　⊙印：採用

	部位・名称	仕様
⊙	MB～給湯器(MB内設置)	⊙ポリブデン管 20
⊙	MB～給水メイン管	⊙ポリブデン管 20
⊙	給水メイン管～各給水栓の給水管	⊙ポリブデン管 13
⊙	給湯器～給湯メイン管	⊙ポリブデン管 16
⊙	給湯メイン管～各給湯栓の給湯管	⊙ポリブデン管 13
⊙	UB天井部ミストカワック用	・ポリブデン管10Aボウズ　⊙CV.CV 15A

給水・給湯設備　注記（全タイプ共通）

⊙	給水管・給湯管は（◎天井配管　・床下配管）とする
	（・天井ヘッダー方式　⊙工場融着先分岐方式（全配管保護管付とする）））
⊙	キッチン，洗面化粧台 給水・給湯 止水栓取付共
・	キッチン，洗面化粧台 給水・給湯 水栓取付部ボックス設置
⊙	キッチン，洗面化粧台の混合水栓は建築工事とする
⊙	キッチン下にて給湯分岐バルブ設置，機器接続含む（食洗器設置）
⊙	キッチン下にて給水分岐バルブ設置，機器接続含む（浄水器設置）
⊙	キッチン下にて給水分岐バルブ設置，機器接続含む(ｹﾞｨｽﾎﾟｰｻﾞｰ自動給水用設置)
⊙	給湯器への給水管・給湯管には逆止弁付バルブ設置
⊙	SKへの給水管の外壁貫通部は未来工業(株)GS-22B-1NOとする（工場融着）
	注）記入無きは特記仕様書参照とする

排水設備　専用部内の仕様（全タイプ共通）　⊙印：採用

	部位・名称	仕様
⊙	キッチンからの排水横引き管	⊙50
⊙	食洗器からの排水横引き管	⊙耐熱性硬質塩ビ管 25
⊙	UBからの排水横引き管	⊙50
⊙	防水パンからの排水横引き管	⊙50
⊙	洗面化粧台からの排水横引き管	⊙40
⊙	便器からの排水横引き管（床上）	⊙75
⊙	便器からの排水横引き管（床下）	⊙75
⊙	合流後の配管サイズ	
	50＋40＝65　50＋65＝65	
	50＋50＝65　トイレ　75	
	排水横引管サイズは，2合流後65とする	

排水設備　注記（全タイプ共通）

・	排水立管より（・半径　・実長）1m以内は耐火二層管とし，以降硬質塩ビ管(VP)とする（・全階　・最下階住戸のみ）
⊙	食洗器排水：キッチン下にて排水分岐チーズ設置とし，排水分岐チーズ及び短管は耐熱塩ビ管HTVPとする
⊙	防水パン接続は内面平滑フレキを使用とする（両端接着タイプ）
⊙	立管スリーブどうしの距離については消防40号省令緩和規定を順守のこと
⊙	洗面化粧台の排水接続部材は設備工事とする
⊙	その他　記入無きは特記仕様書参照とする

取消線

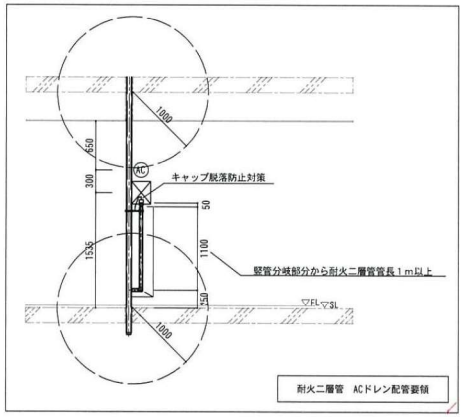

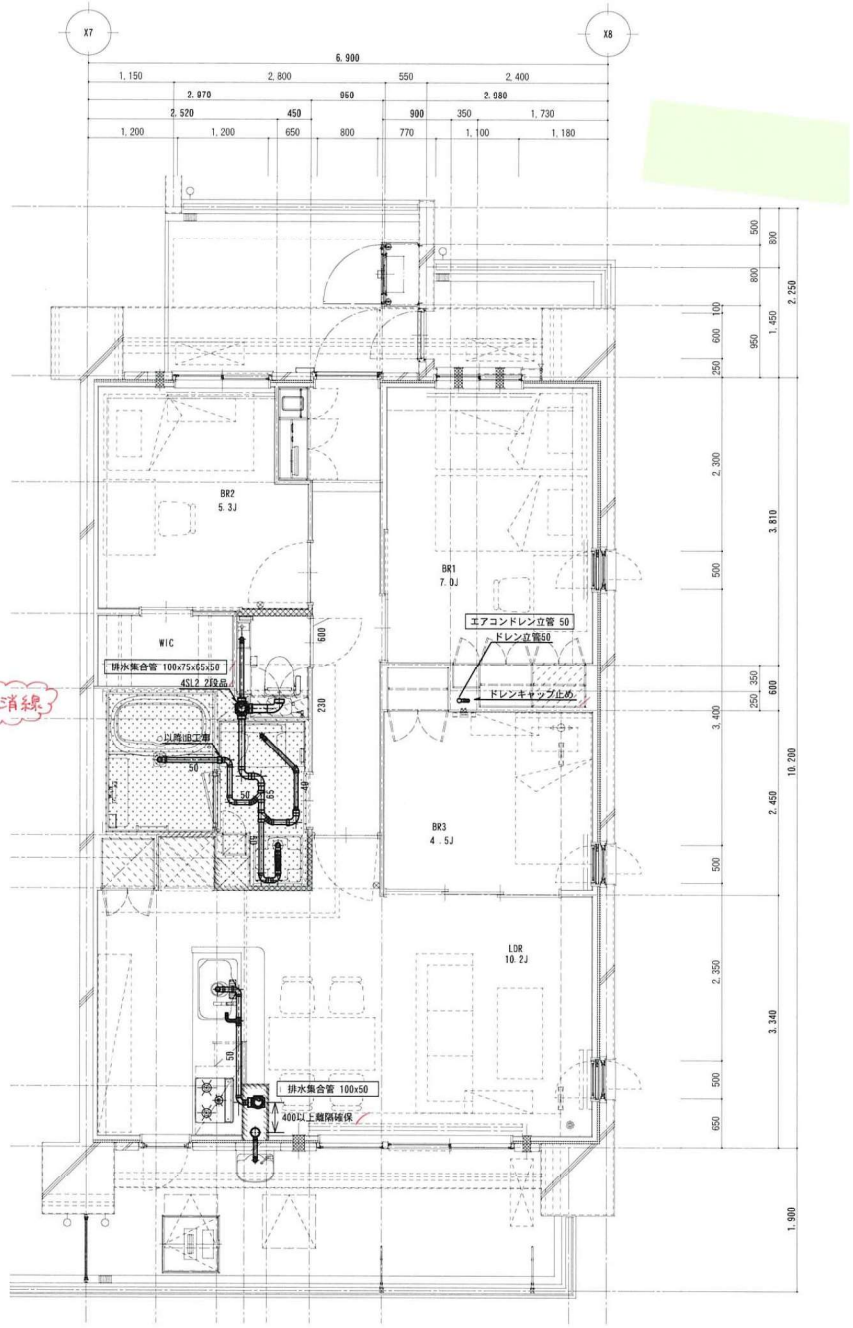

排水設備図

代表となる設計者 不二建設株式会社 一級建築士事務所 (大阪府) 知事登録 第01945号 / 髙藤 謙二 一級建築士 (大 阪) 登 録 第36867号	承認 財田	小林	担当 小倉	日付 2024/11/30	工事名称
その他の設計者 不二建設株式会社 一級建築士事務所 (大阪府) 知事登録 第01945号 / 橋詰 由紀 一級建築士 (大 阪) 登 録 第321259号 / 設備設計一級建築士 (大 阪) 登 録 第 6434号					

図面名称	縮尺	図面番号
給水・排水設備 Aタイプ平面詳細図	1/50 (A2) 1/70 (A3)	M－06－01

ADVANCED ARCHITECTURE